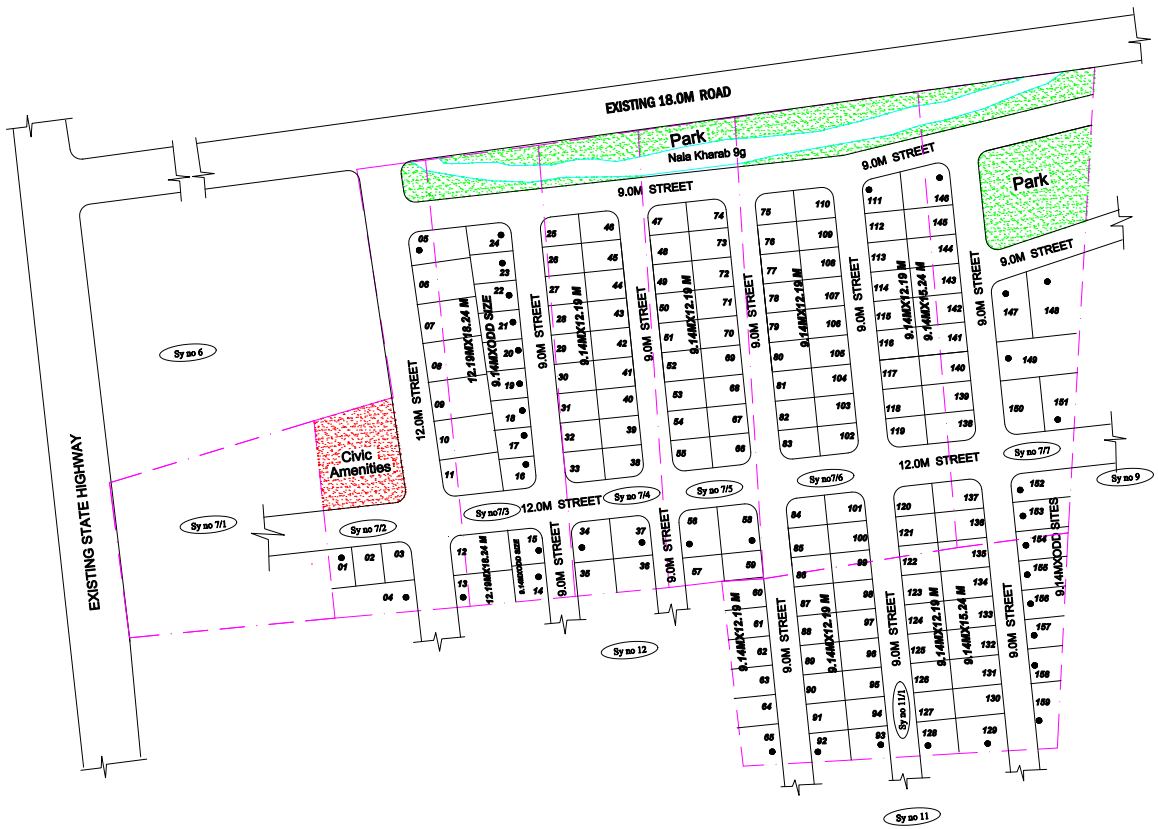

DRAFT PLAN

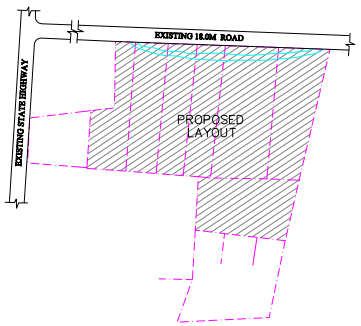

PROPOSED LAND

N

KEY PLAN

NTS

LAND USE ANALYSIS

Sl.No	Land Use	Area Sq.m	%
1.	Residential	19,900.54	54.64
2.	Park & Open space	2,804.30	07.70
3.	Civic Amenities	753.00	02.40
4.	Road	12,796.71	35.26
	Total	36,421.20	100.00

TOTAL EXTENT : 3.642 ha (09 A - 00 G)

KHARAB : (0 A - 09G)

INDEX

Layout Boundary

SITE DETAILS

Sl.No	Dimension		Nos
1.	12.19x 18.28m	——	08
2.	9.14 x 15.24m	——	16
3.	9.14 x 12.19m	——	97
4.	Odd Sites (•)	——	38
	Total	——	159

N

GOVERNMENT OF KARNATAKA

DEPARTMENT OF TOWN & COUNTRY PLANNING

OFFICE OF THE ASSISTANT DIRECTOR OF TOWN & COUNTRY PLANNING, CHIKKABALLAPURA

Assistant Director
Town & Country Planning
Chikkaballapur

Dwg. Title		
	PROPOSED RESIDENTIAL LAYOUT AT SY.NO. 7/2, 7/3, 7/4, 7/5, 7/6, 7/7 & 11/1 OF BELLUTI VILLAGE, KASABA HOBLI, SHIDLAGHATTA TALUK, CHIKKABALLAPUR DISTRICT. EXTENT: 3.642 Hec (09 ACRE 00 GUNTAS) I/F OF	Scale : 1:1000
		Date : JANUARY 2013